

戸建住宅

集合住宅

商用施設


医療福祉施設

教育施設

公共施設

Hi hatch

CEILING ACCESS HATCH

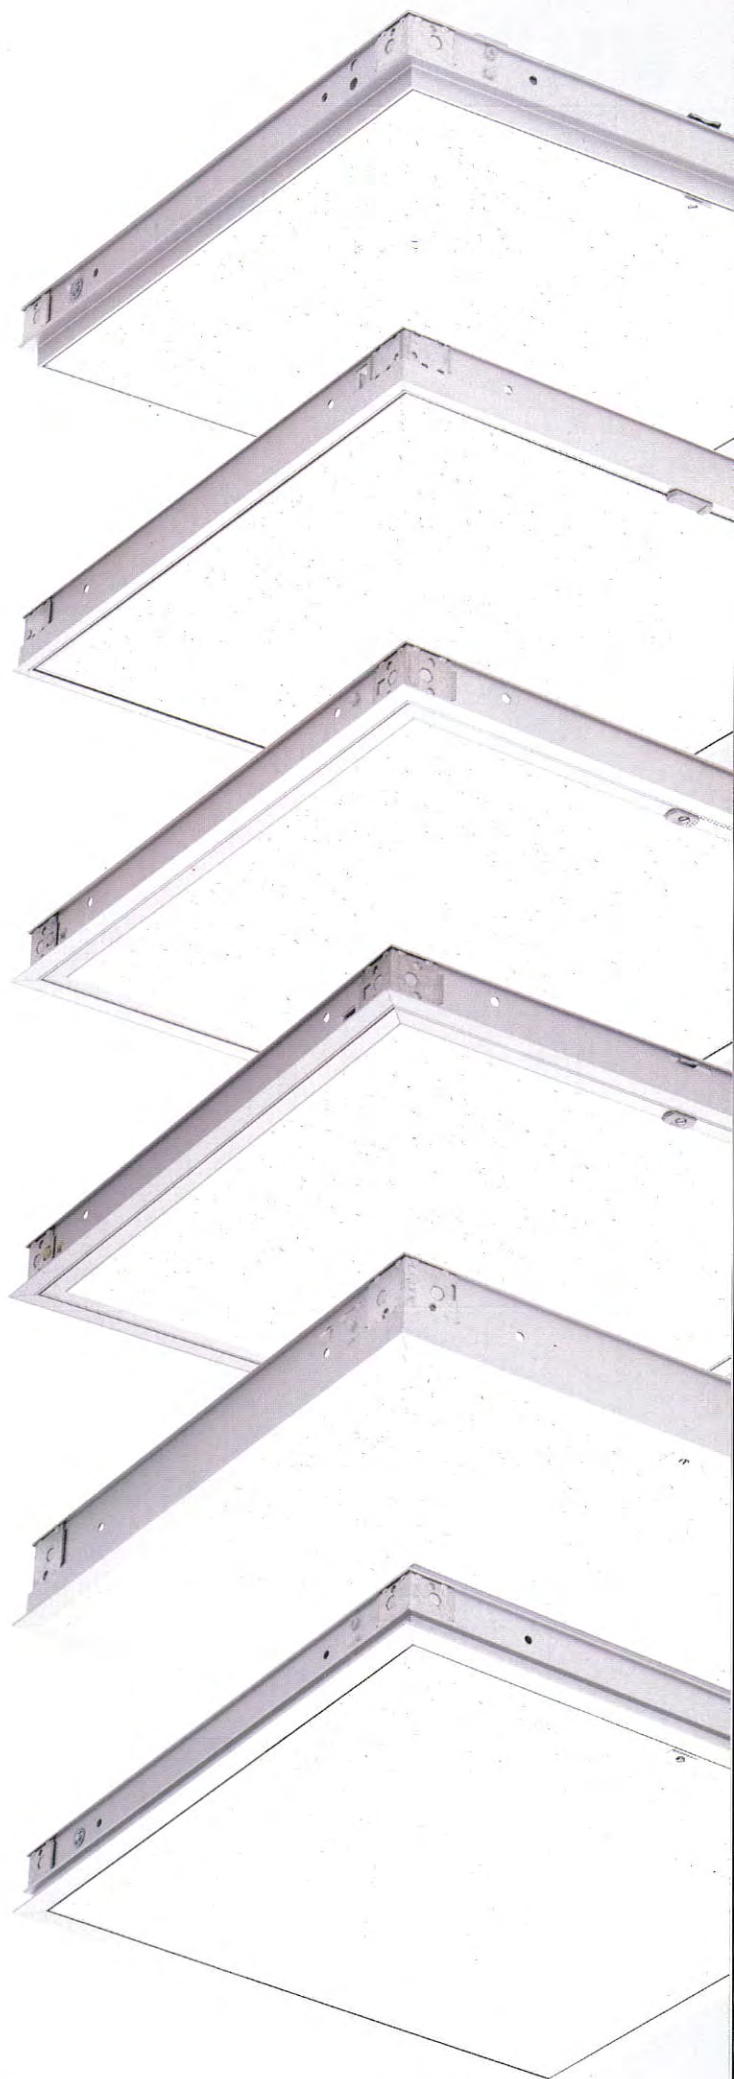

点検口


NAKA

HI HATCH MMII CONCEAL TYPE




Hi-Hatch is valued highly suitable for Public Facility
Certificate No. 971-02600507



SECTION DETAIL S = 1:5

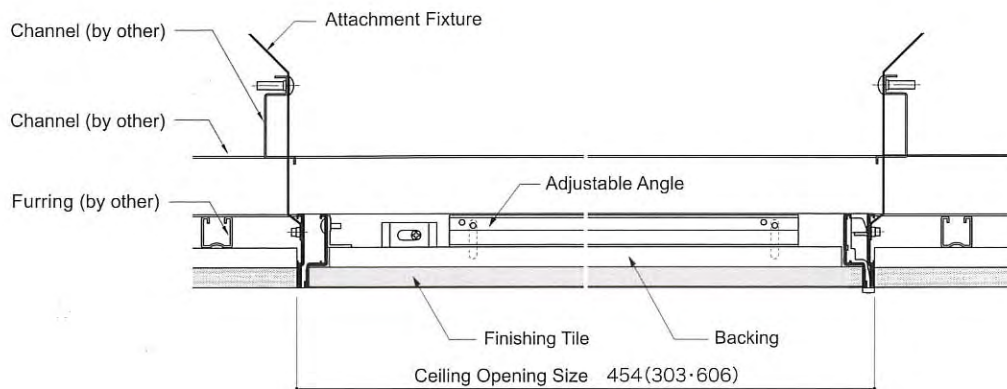

DETAIL

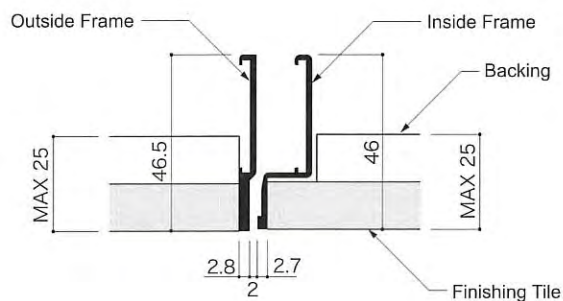

MESUREMENT DETAIL

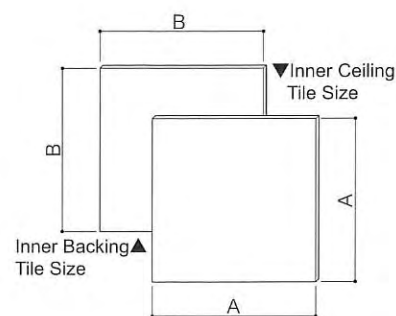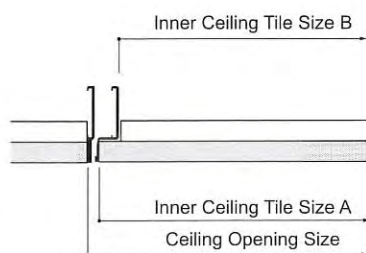

▲Standard Slide Lock

▲Key Lock

SPECIFICATION

Inside Frame / Outside Frame /
Adjustable Angle
Extruded Aluminium with
Anodised Finish (A6063S-T5)

White Colour Anodised Finish



Colour : Ivory White
Size : 454 Only
Model Name : HHMMII454W

		Size (mm)			
SIZE	TYPE	HHMM II -303 (HHMMII-K303)	HHMM II -3060 (HHMMII-K3060)	HHMM II -454 (HHMMII-K454)	HHMM II -606 (HHMMII-K606)
Standard Size		303×303	303×606	454×454	606×606
Ceiling Opening Size		303×303	303×606	454×454	606×606
Inner Ceiling Tile Size A		288×288	288×591	439×439	591×591
Inner Ceiling Tile Size B		262×262	262×565	413×413	565×565


● () for Key Lock Model

HI HATCH
SE
STANDARD TYPE




Hi-Hatch is valued highly suitable for Public Facility
Certificate No. 971-02600507


■ SECTION DETAIL S = 1:5

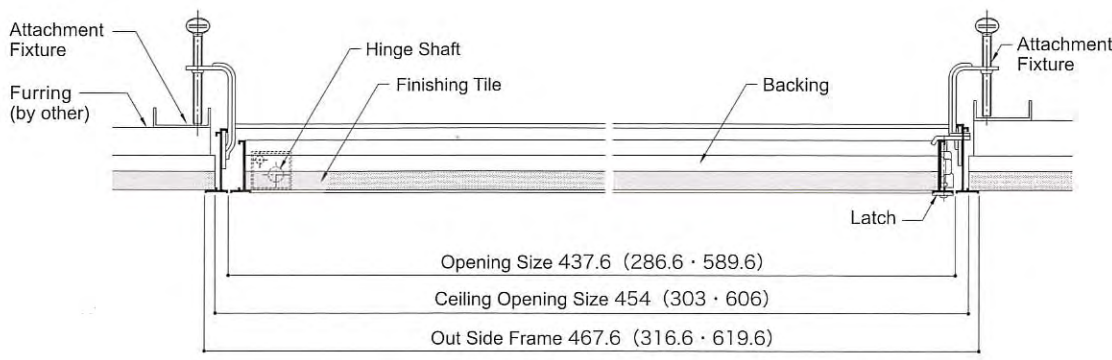

■ DETAIL

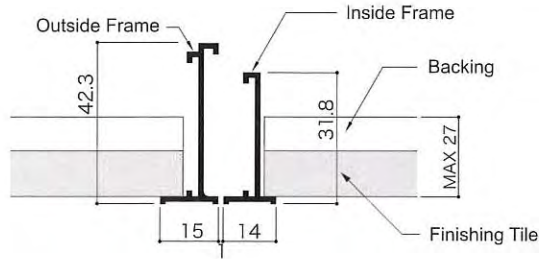

■ MESUREMENT DETAIL

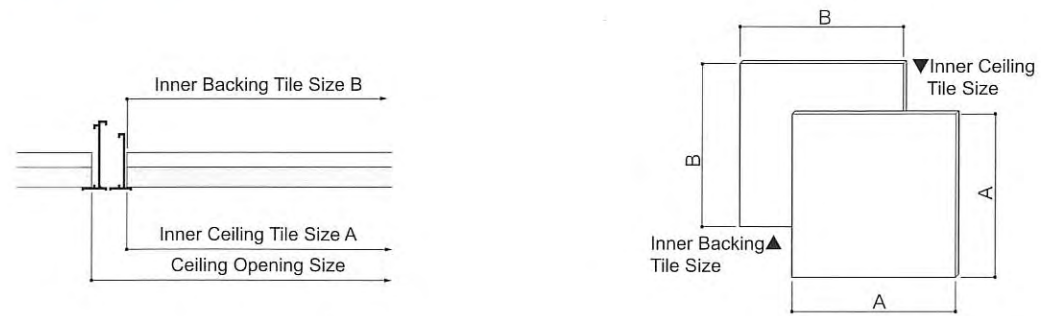

▲Standard Turn Lock

▲Key Lock

■ SPECIFICATION

Inside Frame / Outside Frame
Extruded Aluminium with
Anodised Finish (A6063S-T5)

White Colour Anodised Finish



Colour : Silky White
Size : 303, 454, 606
Model Name : HHSE-303W·454W·606W

		Size (mm)			
SIZE	TYPE	HHSE-303 (HHSE-K303)	HHSE-3060 (HHSE-K3060)	HHSE-454 (HHSE-K454)	HHSE-606 (HHSE-K606)
Standard Size		303×303	303×606	454×454	606×606
Ceiling Opening Size		305×305	305×608	456×456	608×608
Inner Ceiling Tile Size A		264×264	264×567	415×415	567×567
Inner Ceiling Tile Size B		264×264	264×567	415×415	567×567

● () for Key Lock Model